


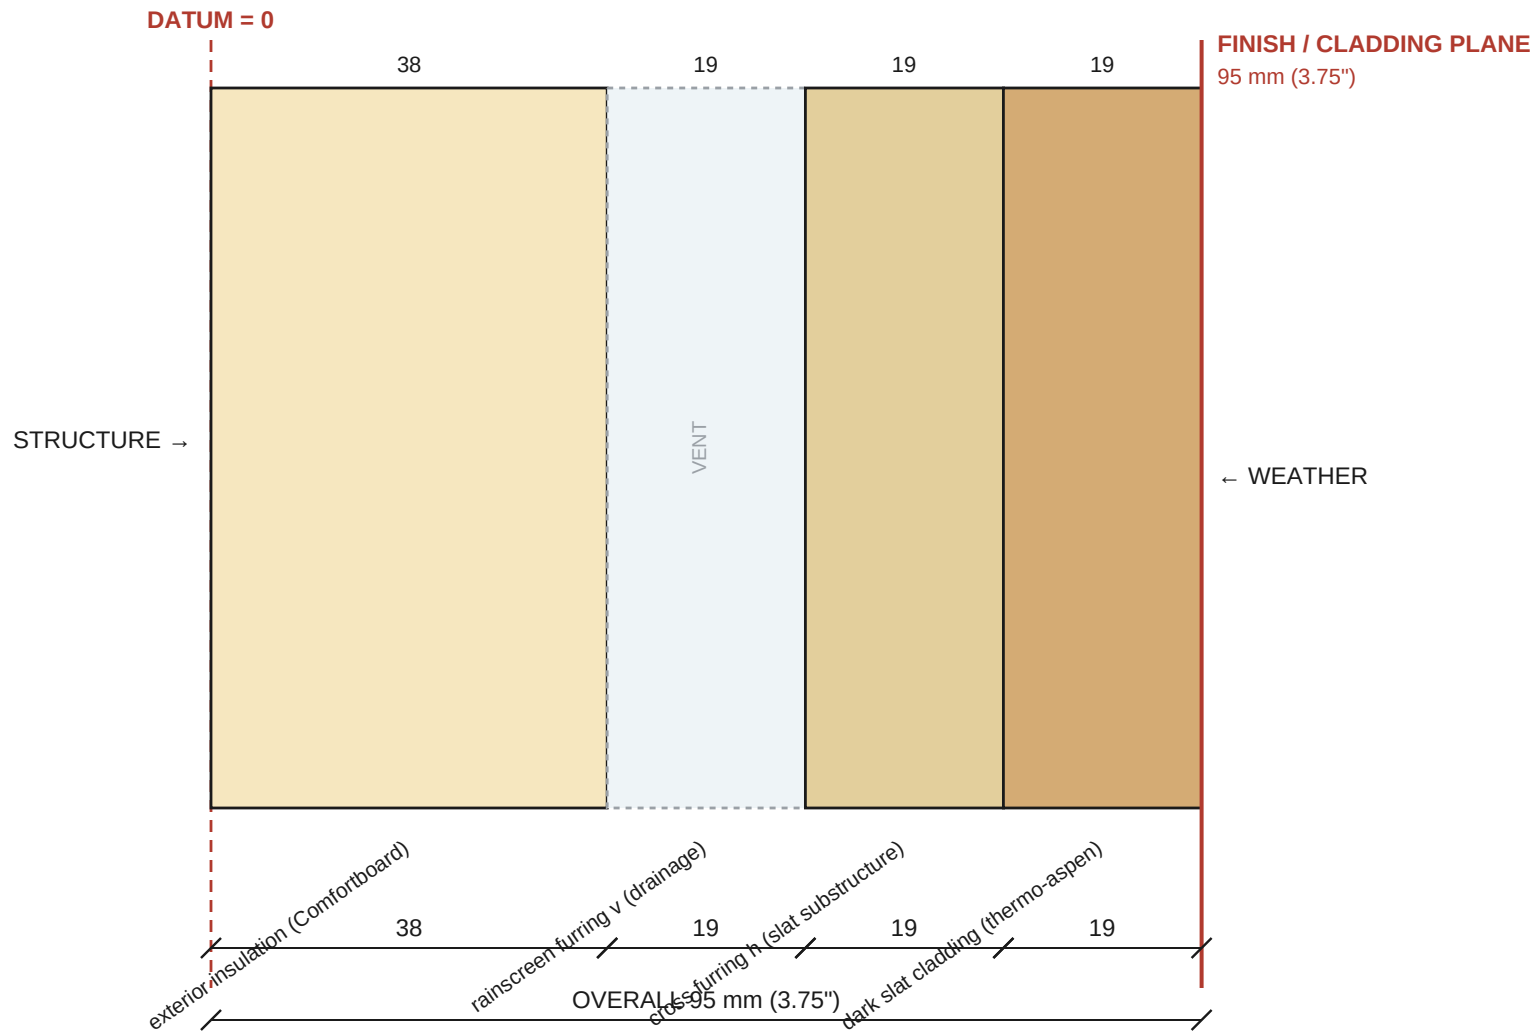

WALL SECTION — outdoor rainscreen envelope

datum: exterior face of 1/2" ZIP sheathing · horizontal = OUTWARD from datum

NOT TO SCALE — do not measure print; use figured dims · generated by sauna_engine