


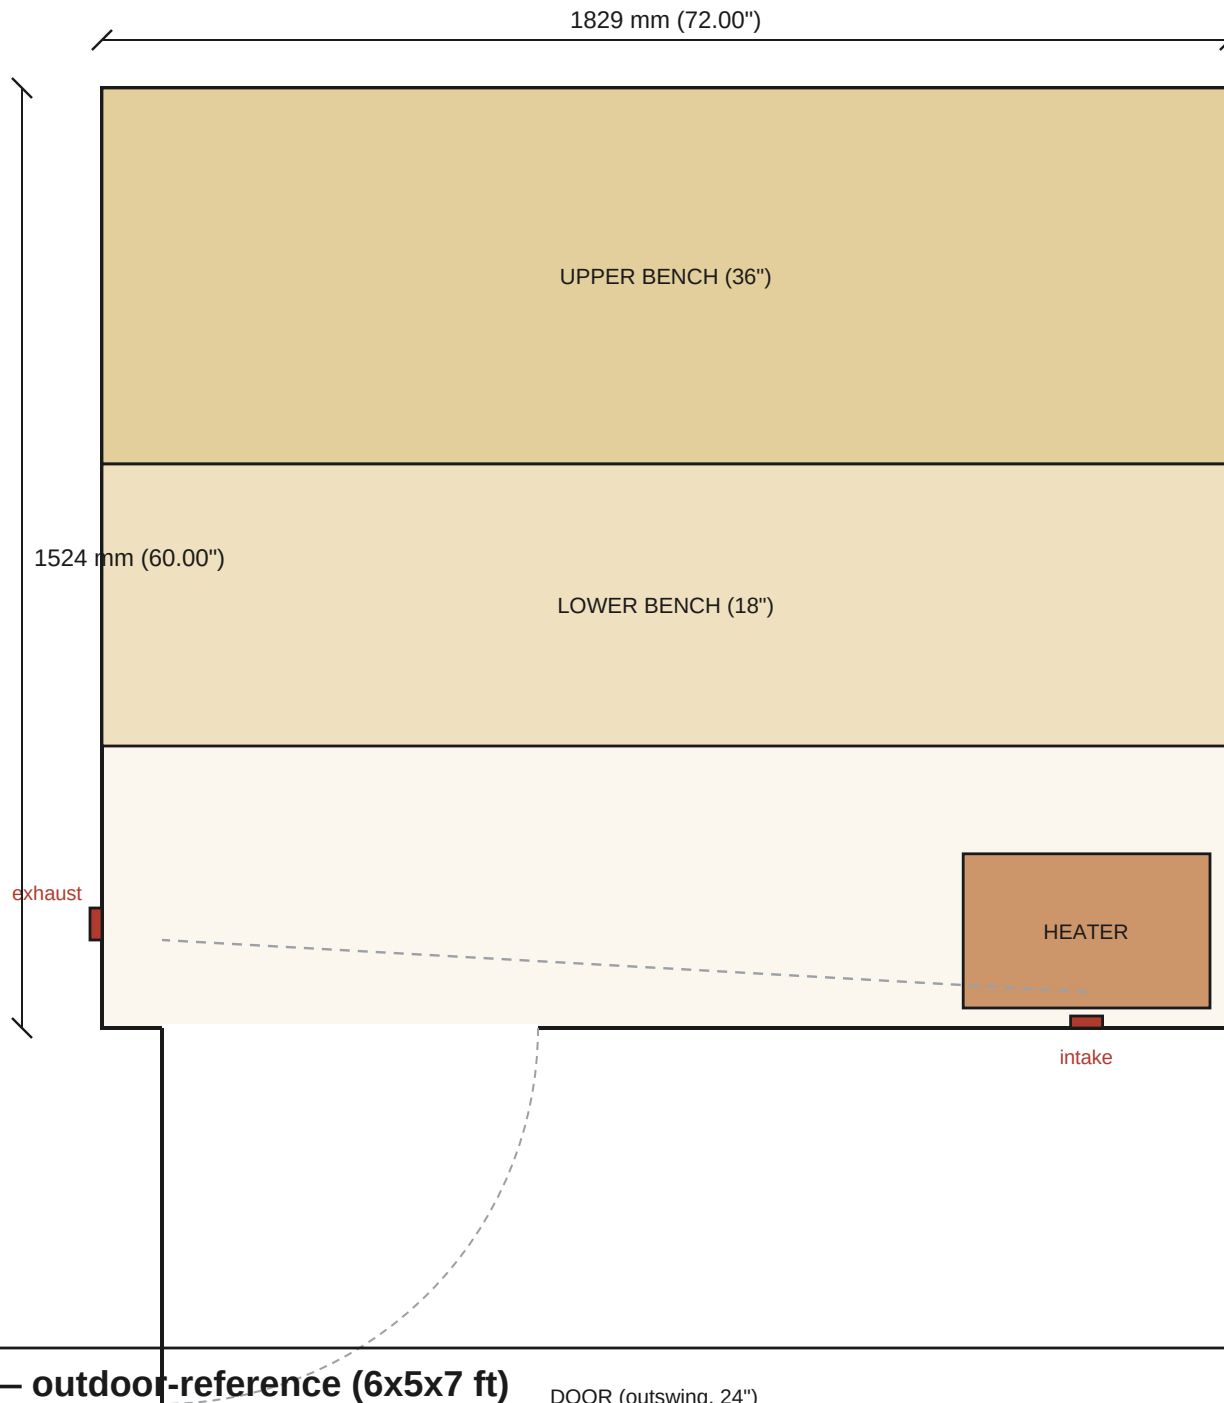


FLOOR PLAN — outdoor-reference (6x5x7 ft)

interior 1829 x 1524 mm · ceiling 2134 mm · plan view

DOOR (outswing, 24")

NOT TO SCALE — do not measure print; use figured dims · generated by sauna_engine


A-0

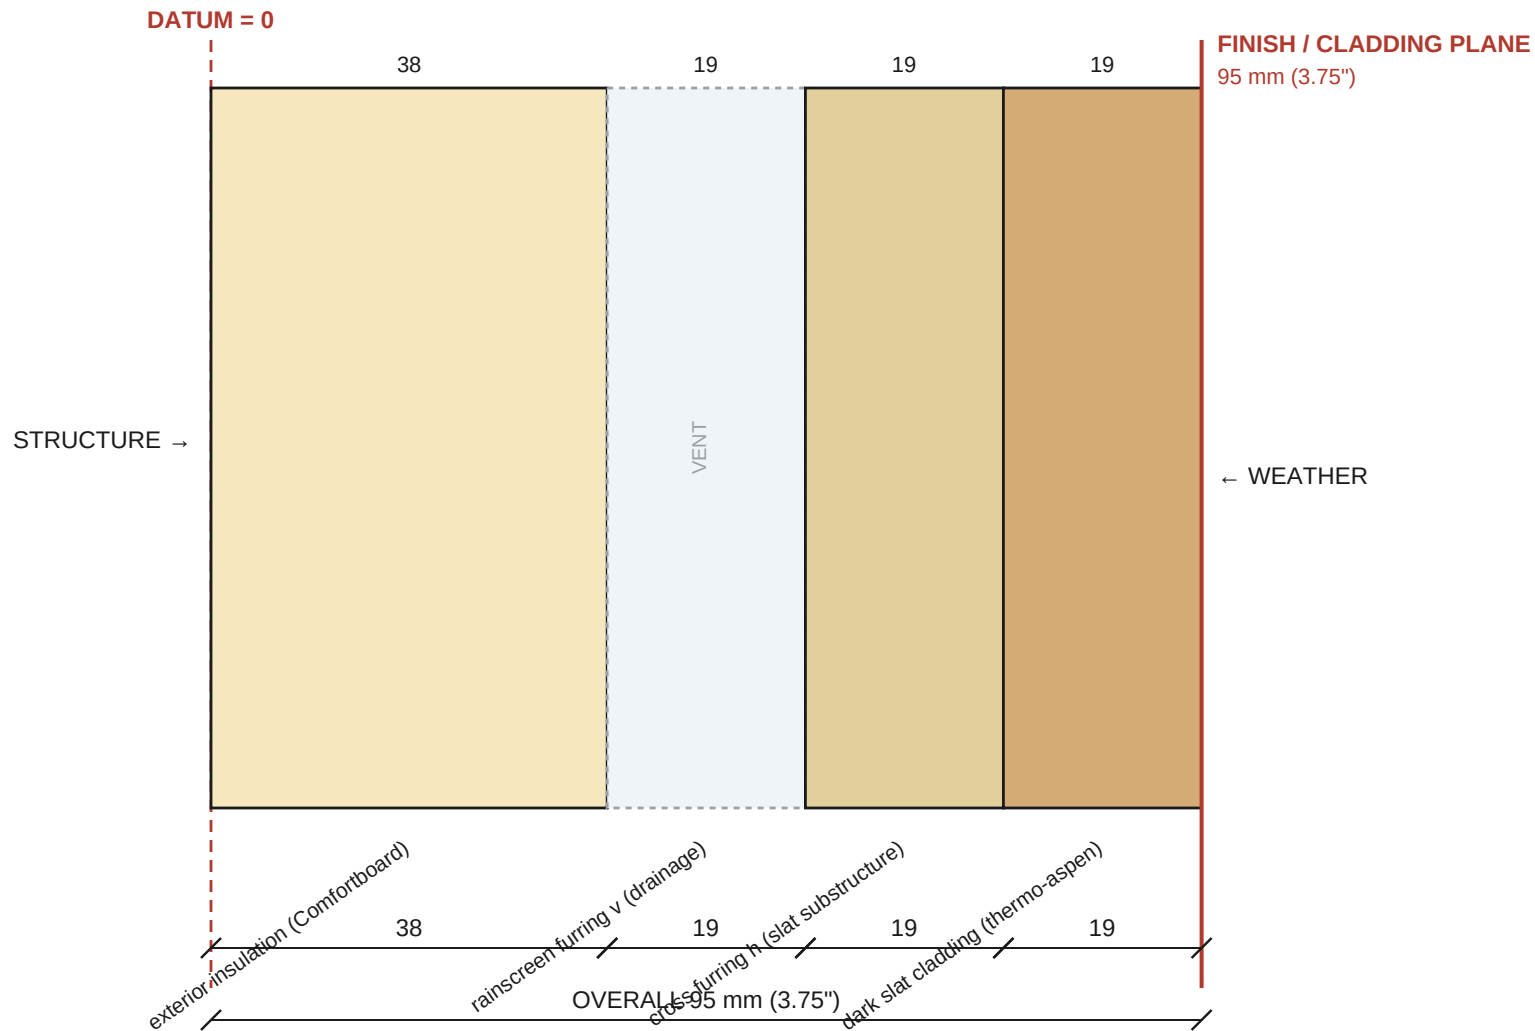

WALL SECTION — outdoor rainscreen envelope

datum: exterior face of 1/2" ZIP sheathing · horizontal = OUTWARD from datum


NOT TO SCALE — do not measure print; use figured dims · generated by sauna_engine

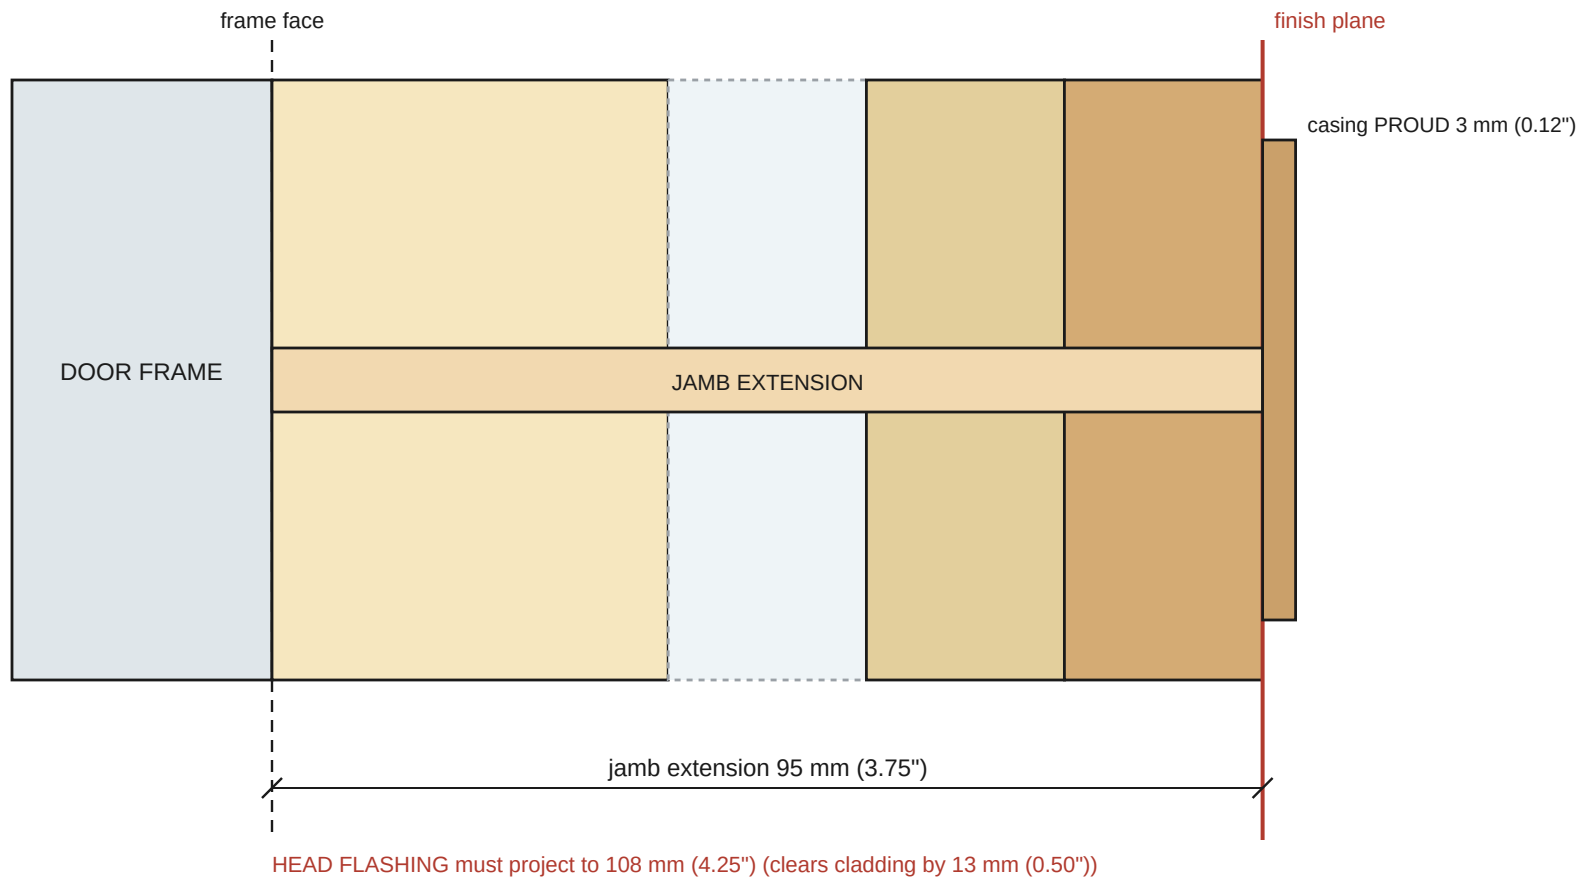

DOOR JAMB — plan detail

frame anchored to structure; jamb extension bridges to finish plane

NOT TO SCALE — do not measure print; use figured dims · generated by sauna_engine

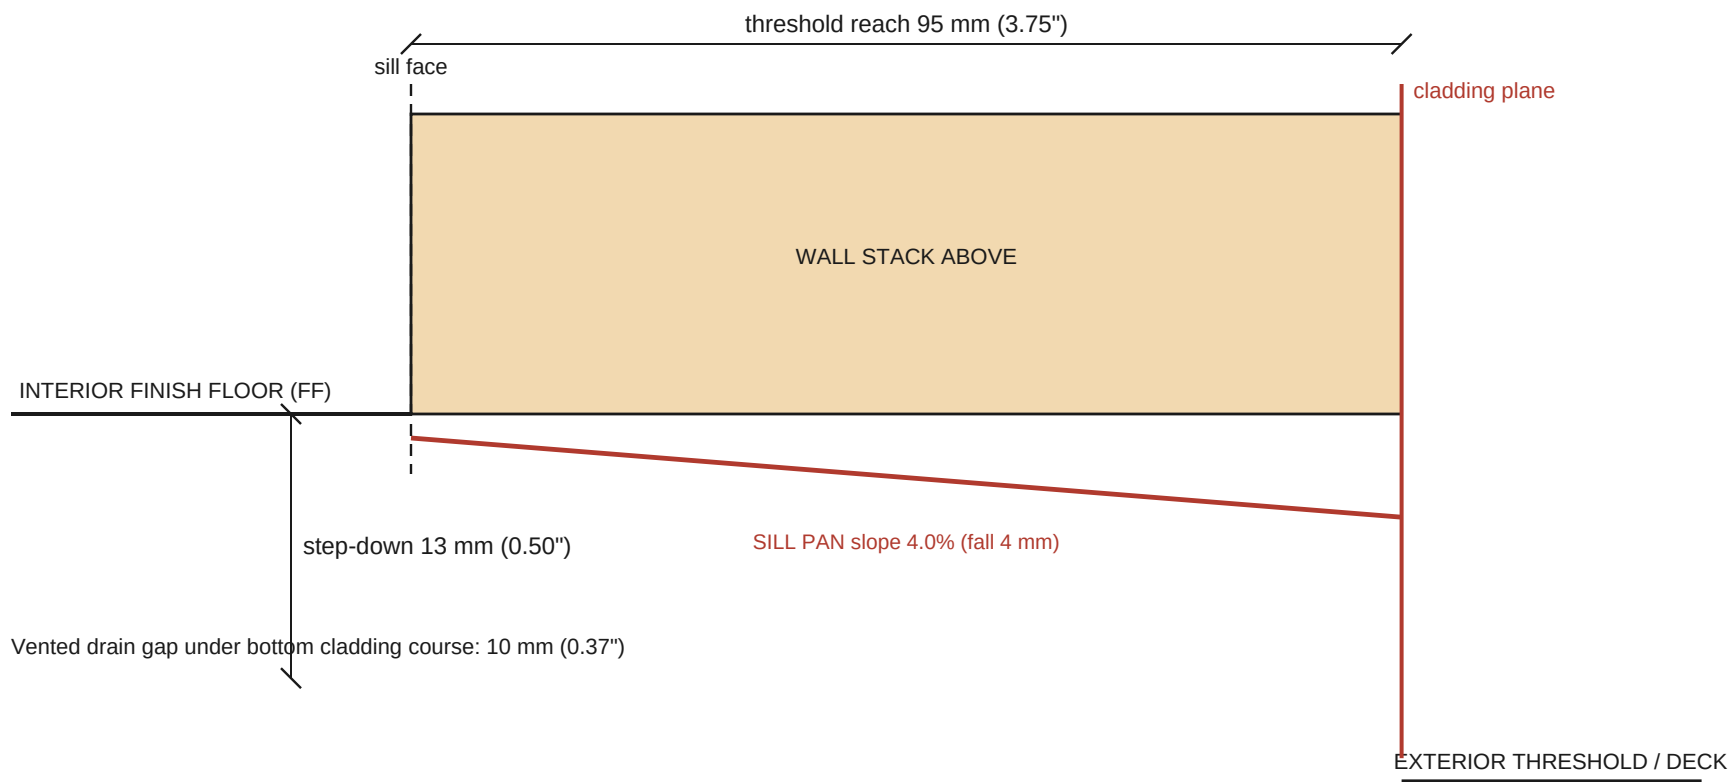

THRESHOLD / SILL — section detail

three planes meet; pan slopes out, step-down keeps water outside

NOT TO SCALE — do not measure print; use figured dims · generated by sauna_engine